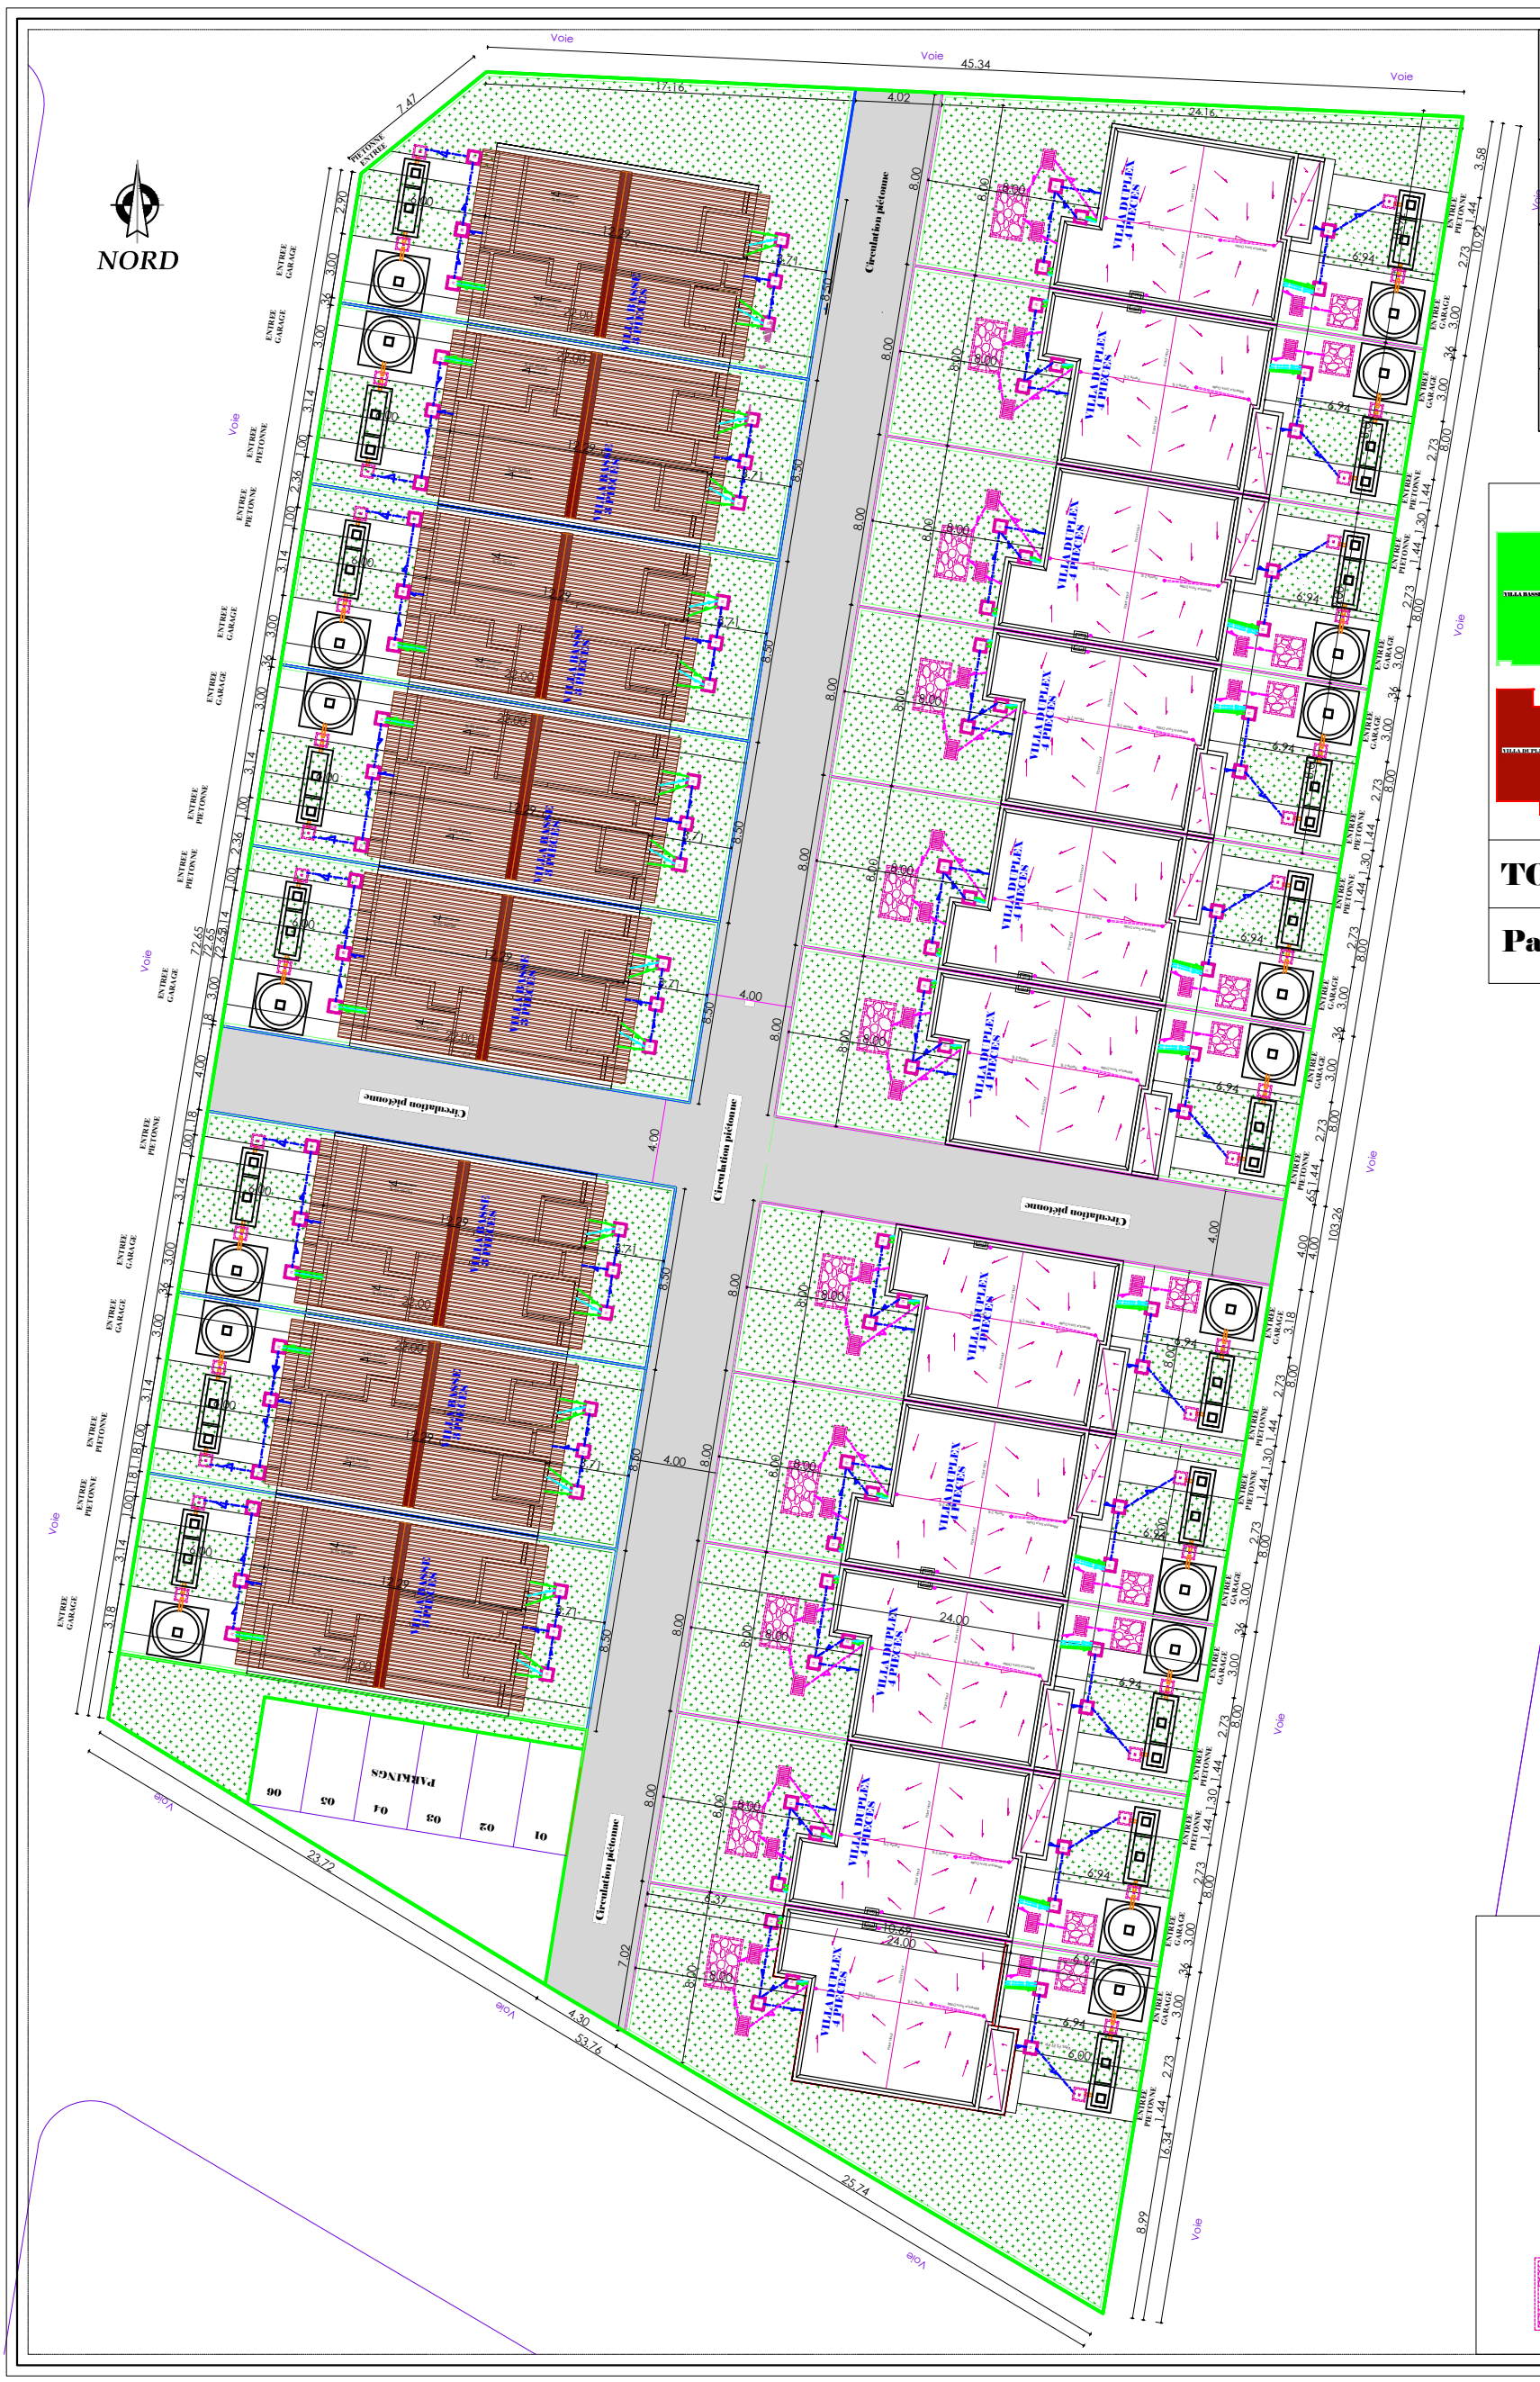

PROPRIETE DE

M. YORO SAKY FRANCK OLIVIER

SUR LES LOTS :518 à 528; Ilot :53

ACD N°:22-1114/MCLU/DGUF/DDU/COD-AO/ TCX Du 09/12/2022

TF N° 21069 I DE SONGON

CNOA

CABINET HUYA-KOUADIO Raoul
Architecte D.P.L.G.
Cel: 01-01- 54-40-44
Email : carchuyak@gmail.com

PROJET DE CONSTRUCTION DE

- 11 VILLAS DUPLEX 4 PIECES

- 08 VILLAS BASSE 3 PIECES

PLAN DE MASSE

PC		PLAN N° 01

Date: Février 2025

ECHELLE : Format A3

VILLA BASSE 3 PIECES : 08

VILLA DUPLEX 4 PIECES : 11

TOTAL : 19 logements

Parkings : 06

Assainissement

EU	Eaux Usées
EV	Eaux Vannes
EU+EV	Eaux Usées+Eaux Vannes
EP	Eaux Pluviales
R	Regard de visite(60x60)
R	Regard de visite(80x80)
R	Regard à Grille Eaux Pluviales (40x60)
	Puit filtrant EP