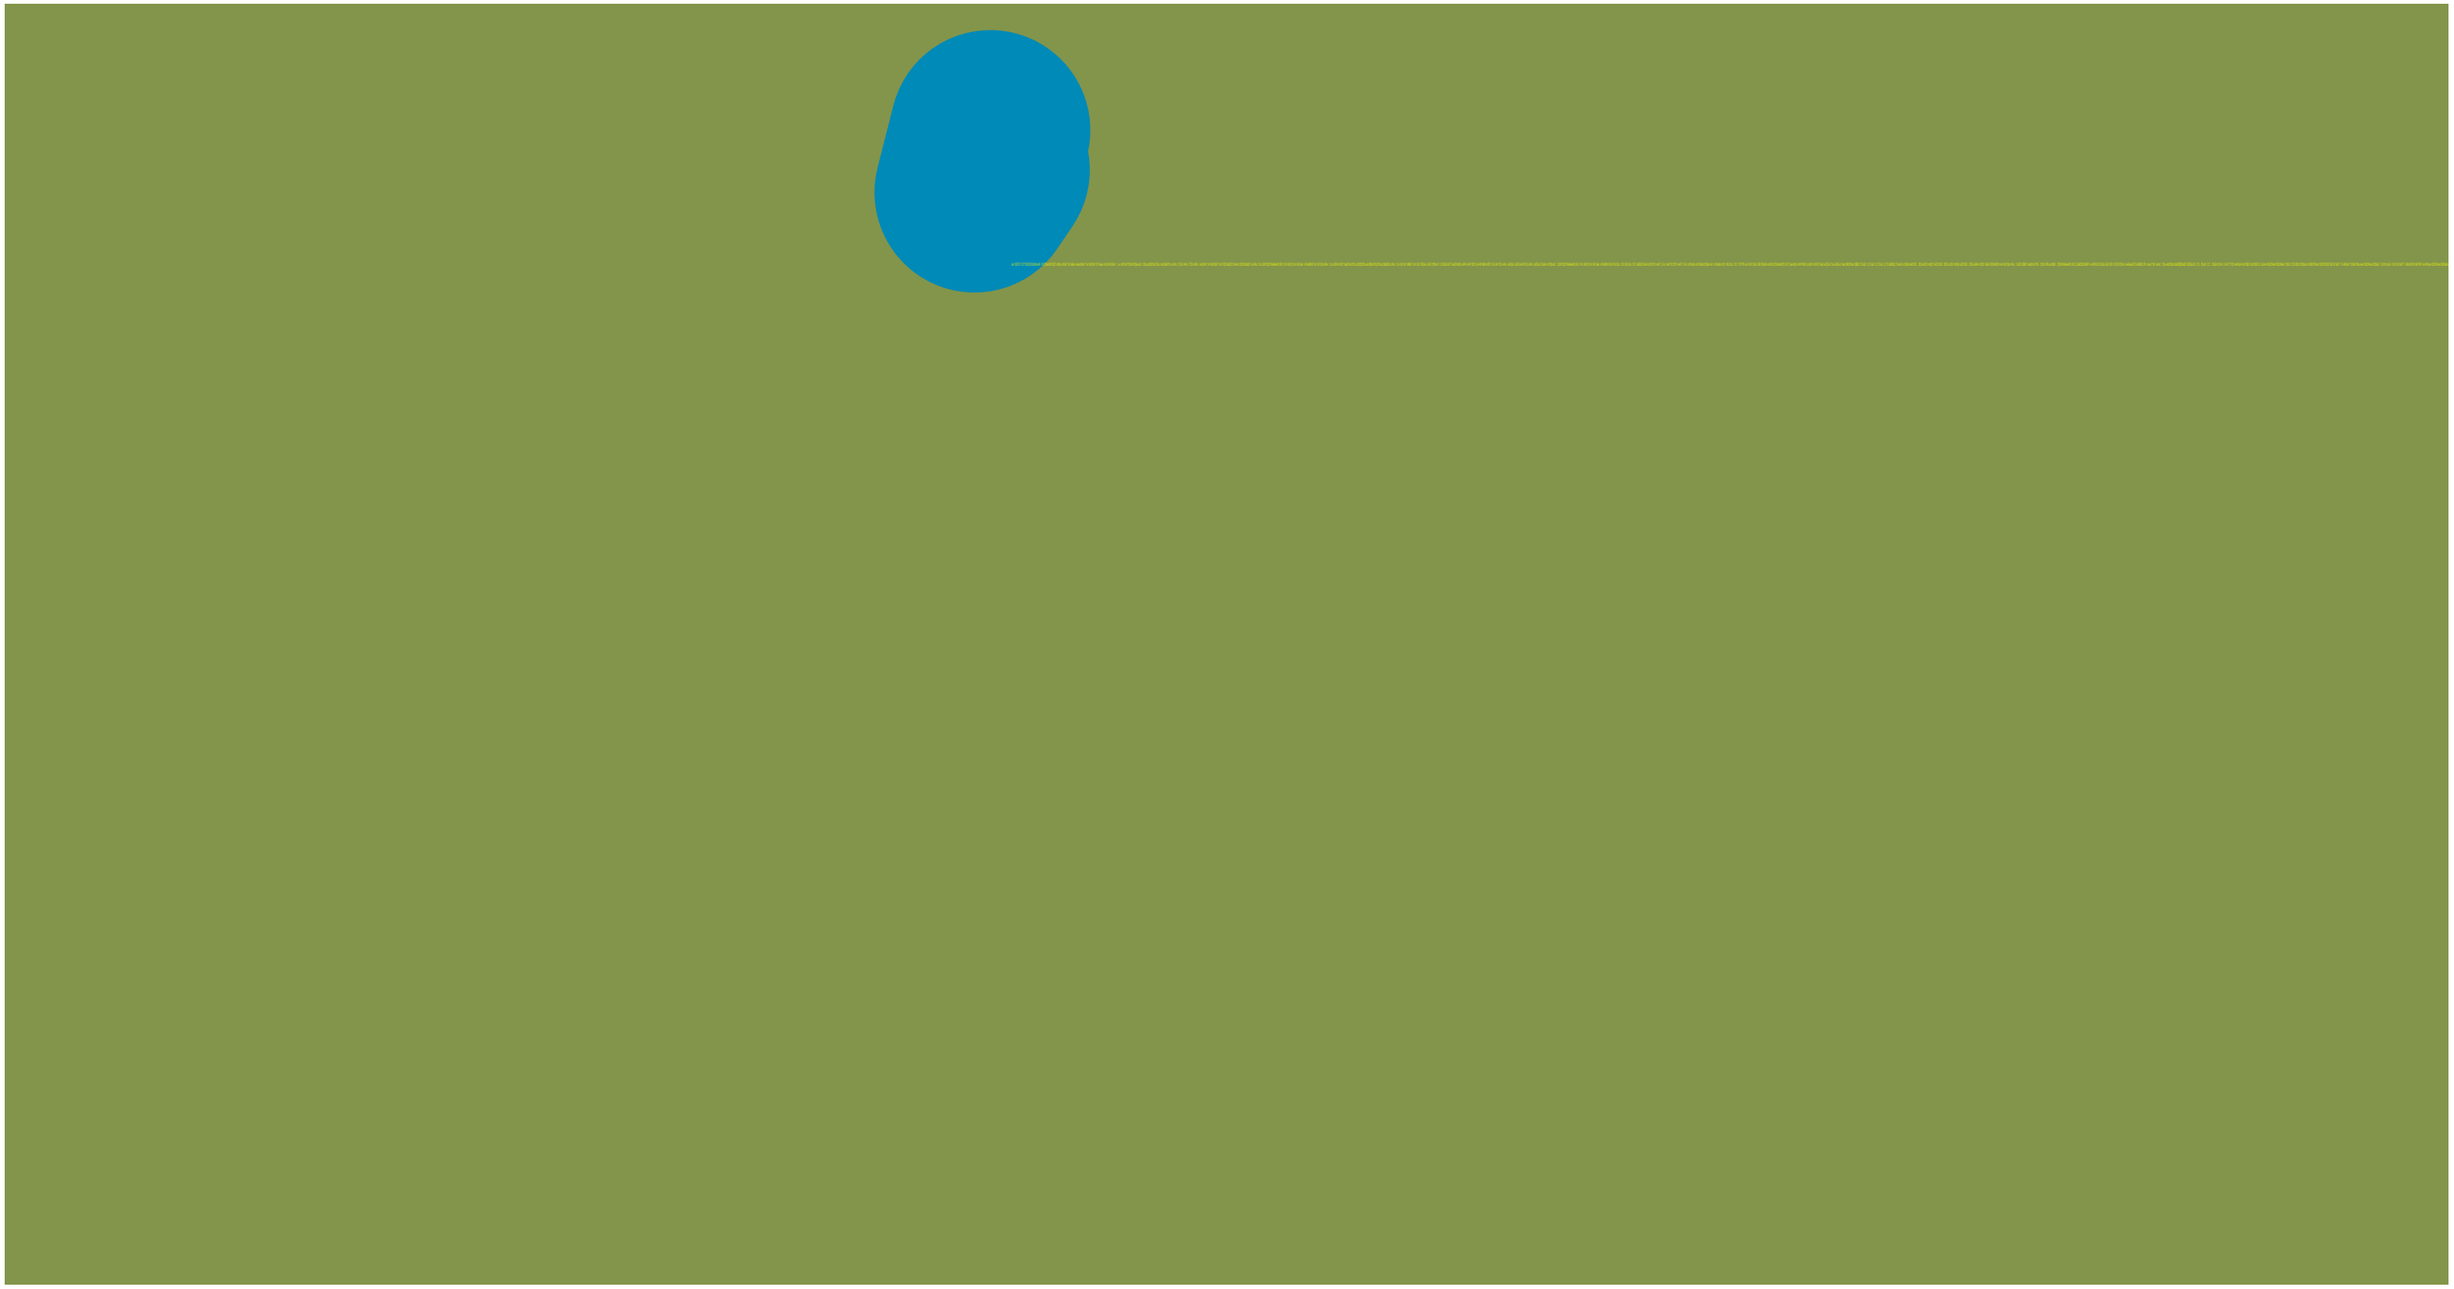

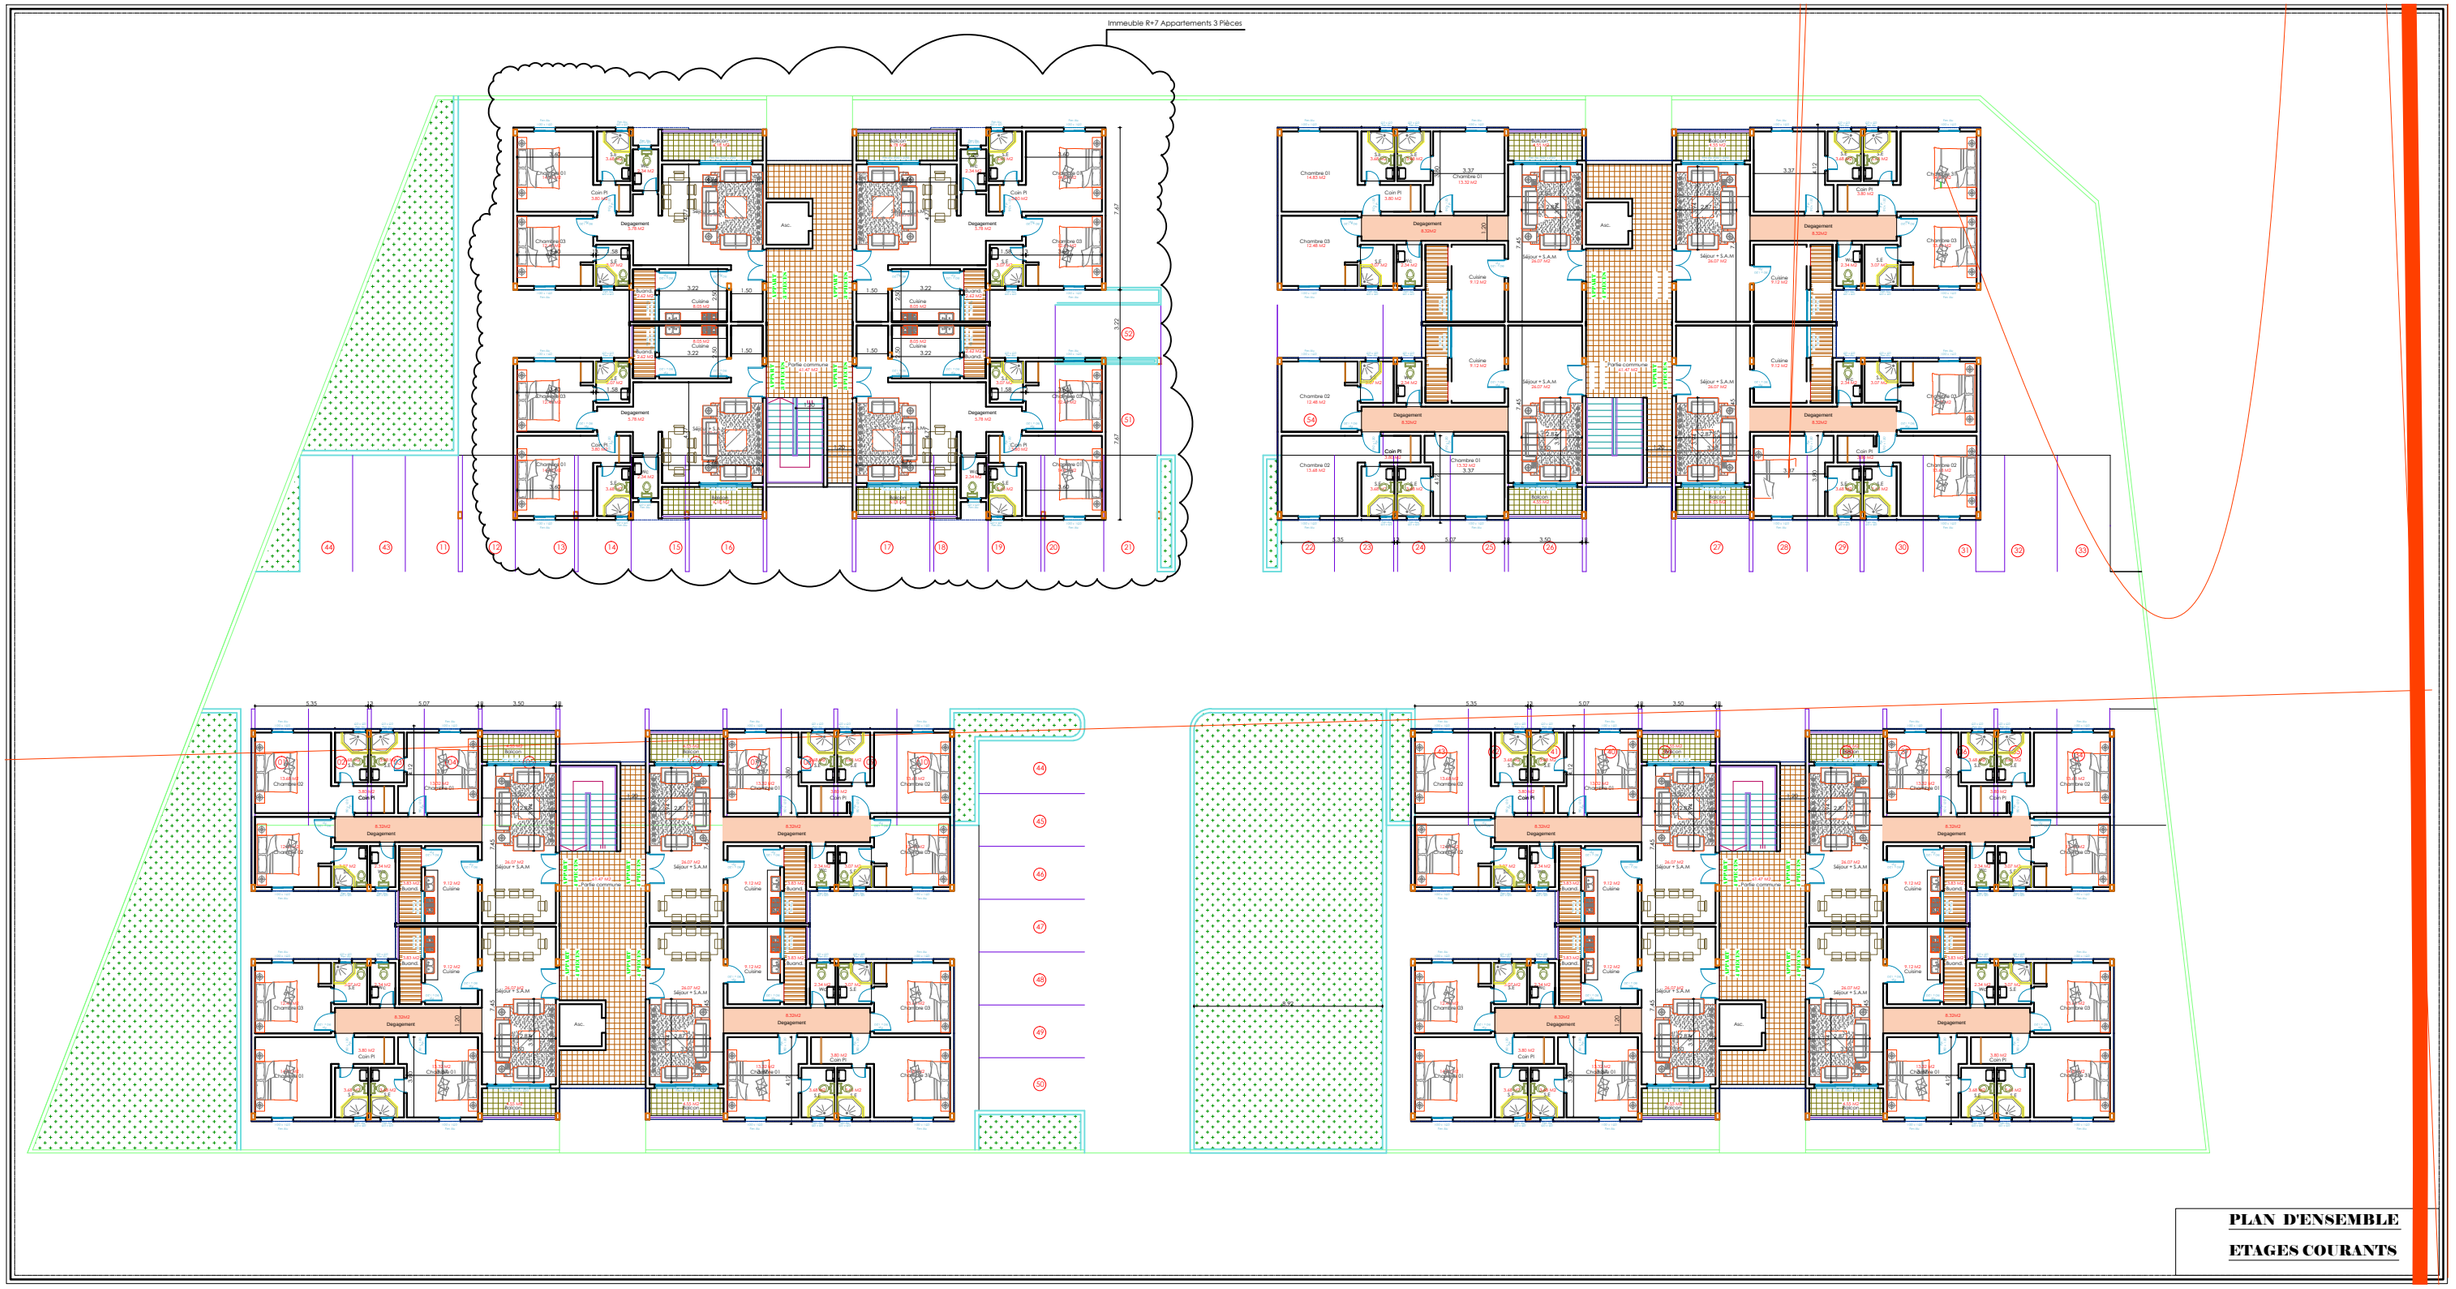

PLAN D'ENSEMBLE

ETAGES COURANTS

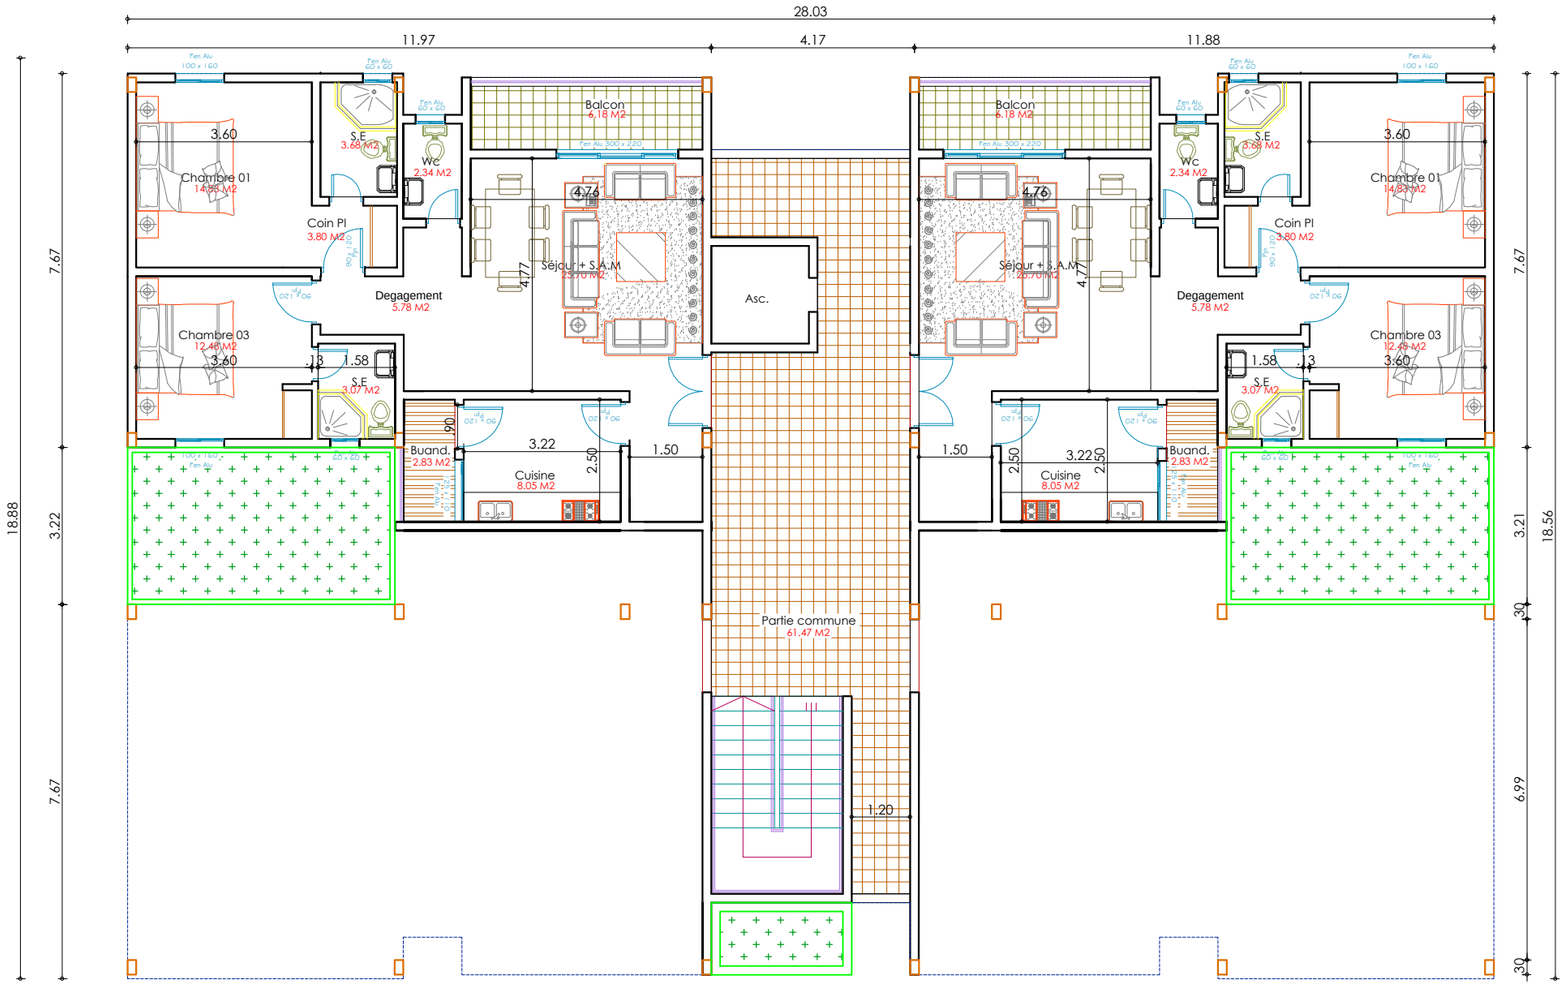

Désignation des locaux	Surfaces
APPARTEMENT 3 PIECES	
Terrasse avant	6.18
Séjour + Salle à manger	25.70
Degagement	5.78
Cuisine	8.81
Buanderie	2.83
Wc	2.34
Chambre 01	14.83
Salle d'eau	3.68
Coin Placard	3.80
Chambre 02	12.48
Salle d'eau	3.07
Surfaces utiles	89,5M2

Désignation des locaux	Surfaces
PARTIE COMMUNE	
Terrasse avant	61.47
Surfaces utiles	61.47 M2

TOTAL PALIER
(89,5 X 2) + 61.47 = 240,49 m2

IMMEUBLE R + 7

PLAN DU REZ-DE-CHAUSSEE

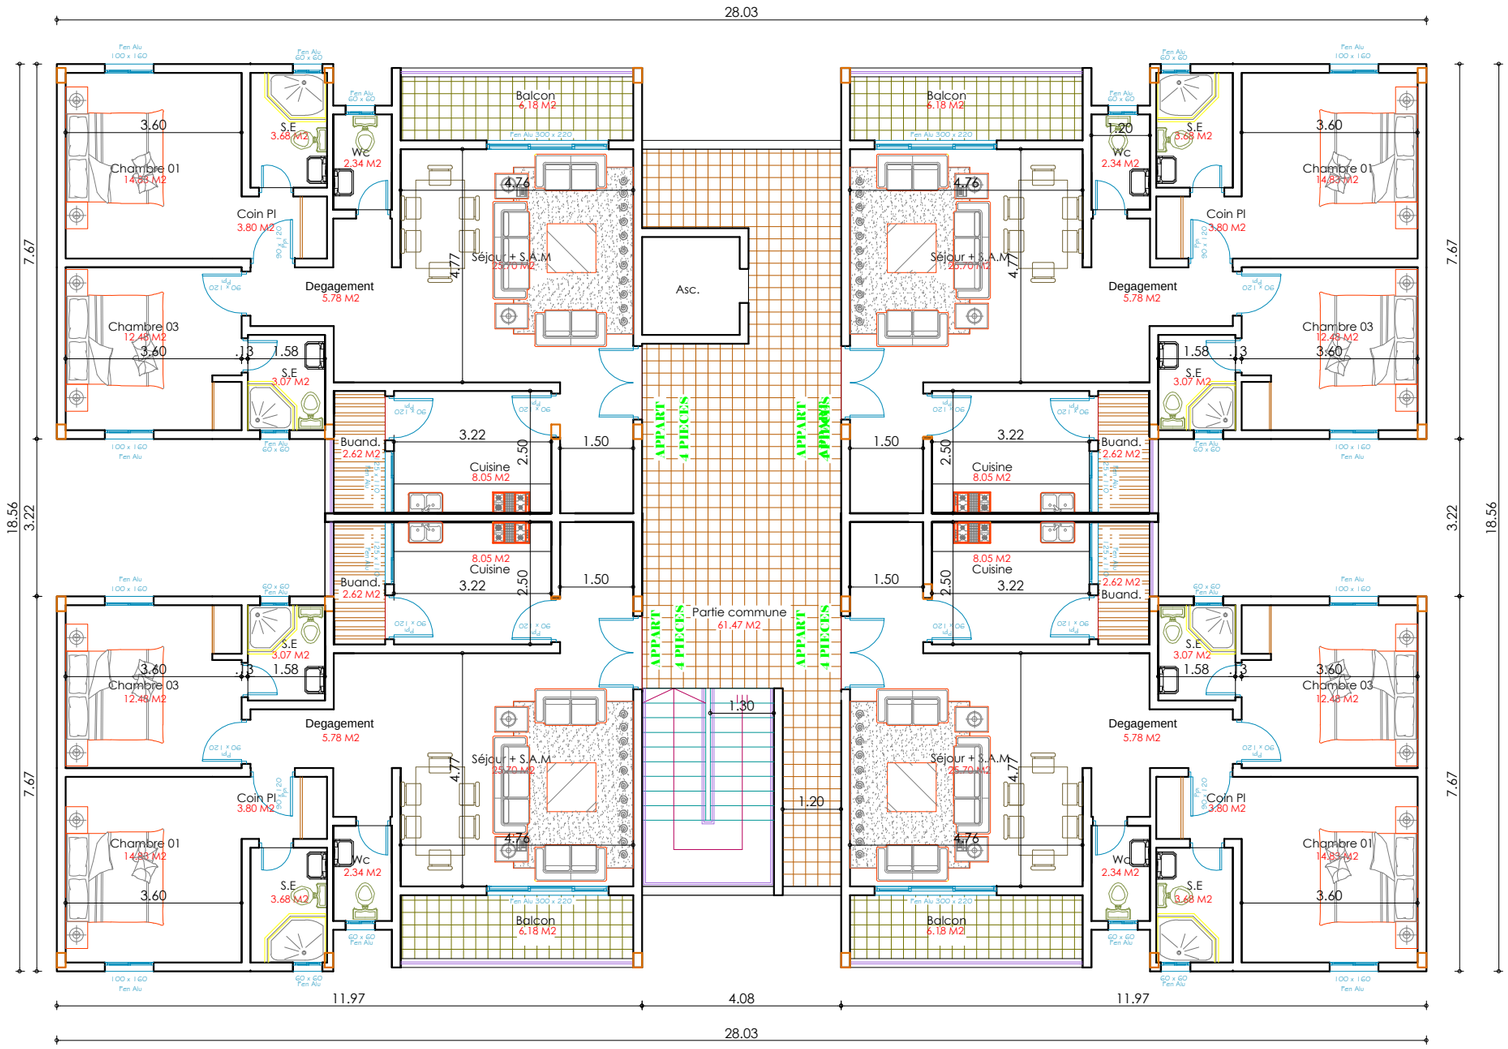

Désignation des locaux	Surfaces
APPARTEMENT 3 PIECES	
Terrasse avant	6.18
Séjour + Salle à manger	25.70
Degagement	5.78
Cuisine	8.05
Buanderie	2.62 M2
Wc	2.34
Chambre 01	14.83
Salle d'eau	3.68
Coin Placard	3.80
Chambre 02	12.48
Salle d'eau	3.07
Surfaces utiles	89,5M2

Désignation des locaux	Surfaces
PARTIE COMMUNE	
Terrasse avant	61.47
Surfaces utiles	61.47 M2

TOTAL PALIER
(89.50 X 4) + 61.47 = 419,47 m2

IMMEUBLE R + 7

PLAN ETAGE COURANT